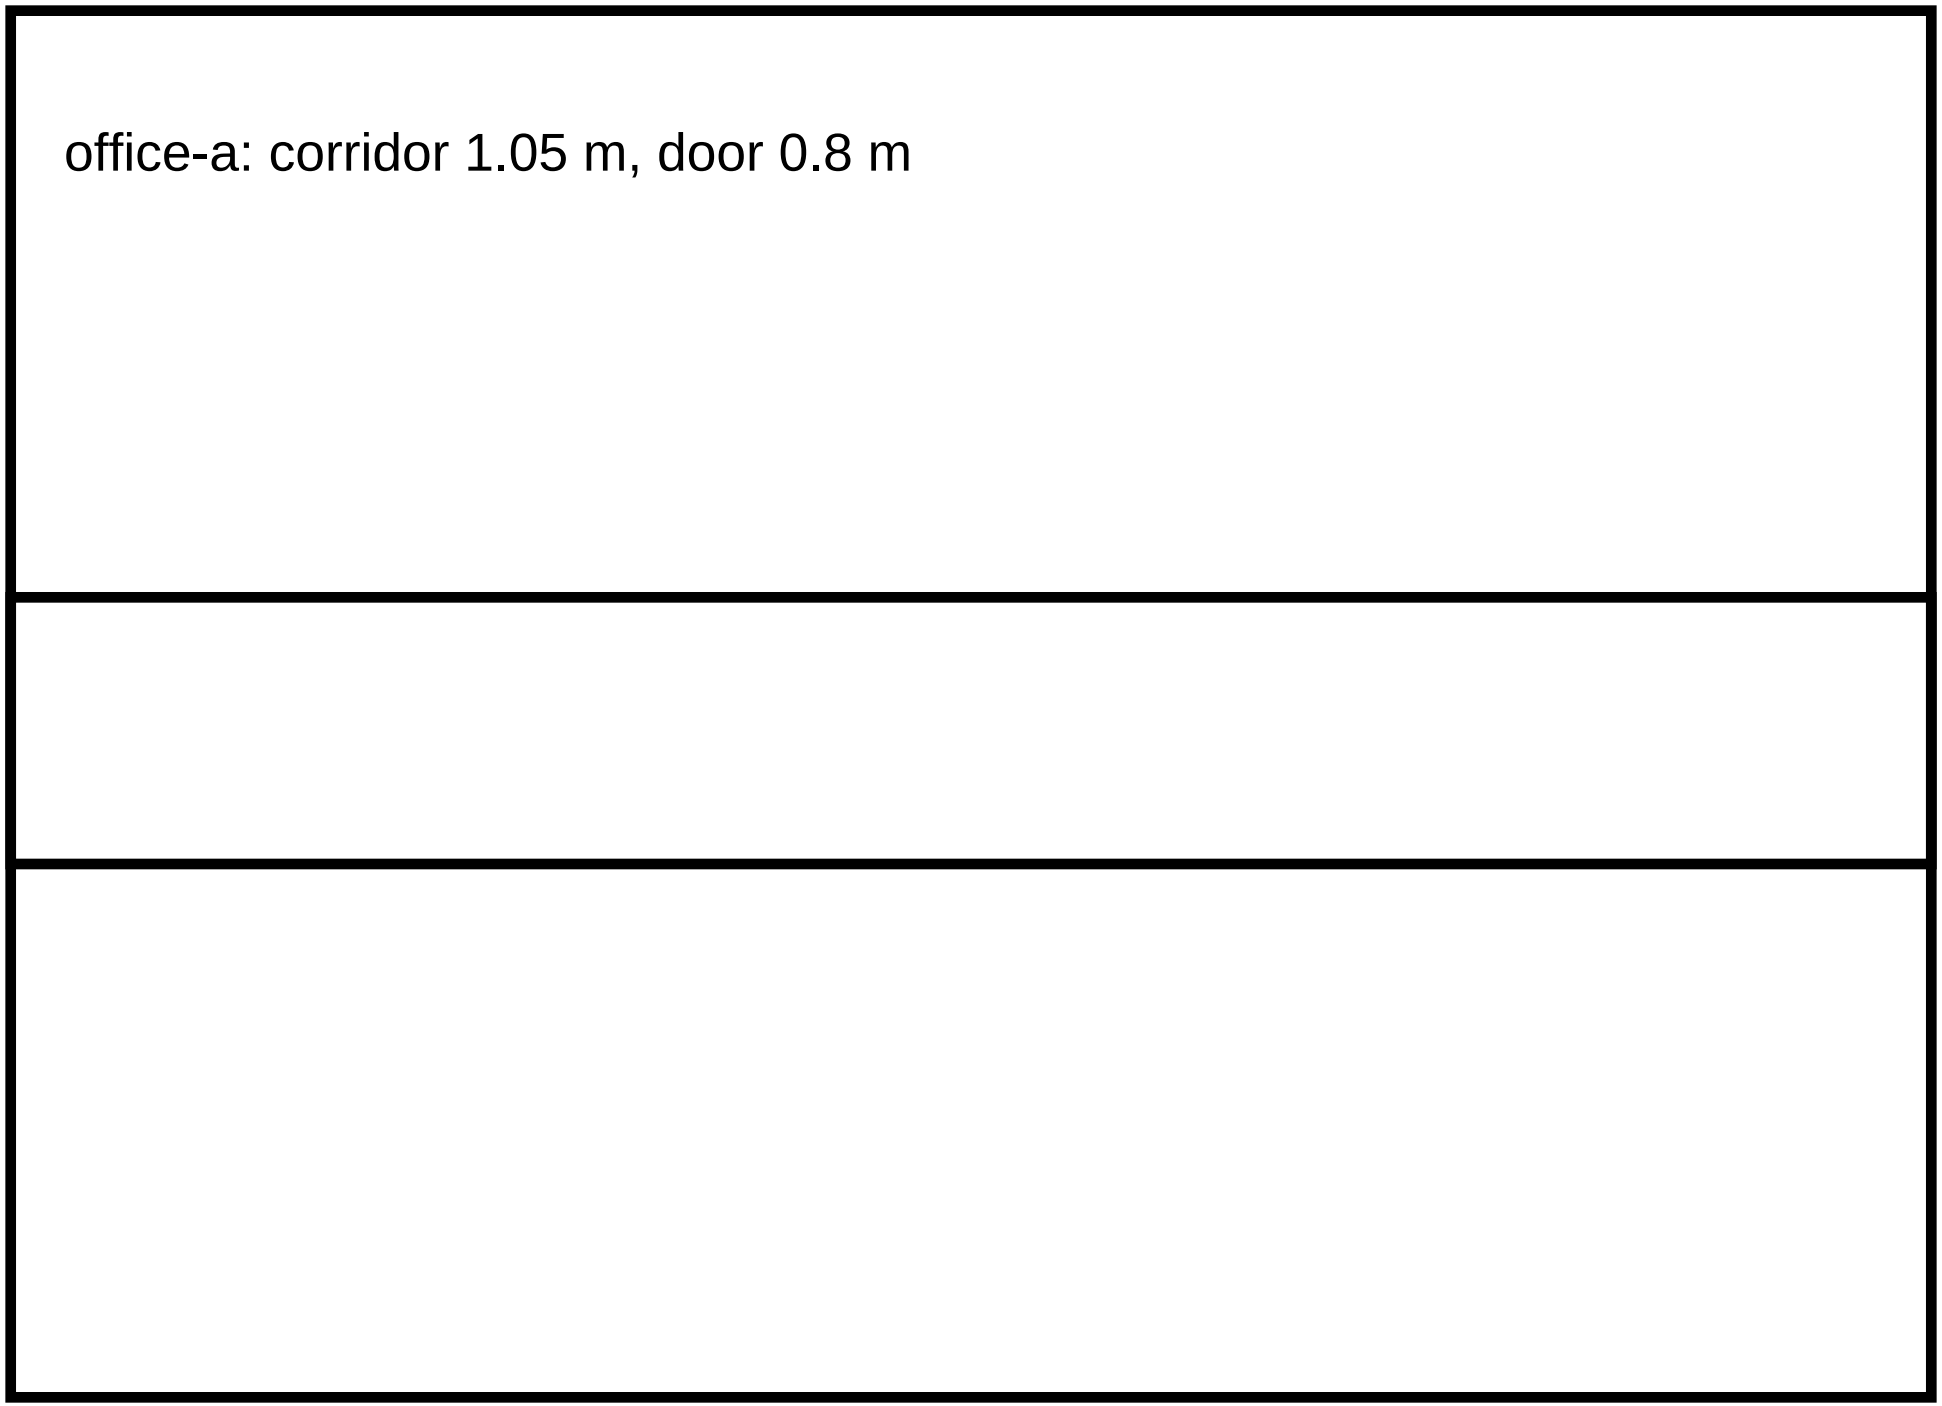
office-a: corridor 1.05 m, door 0.8 m

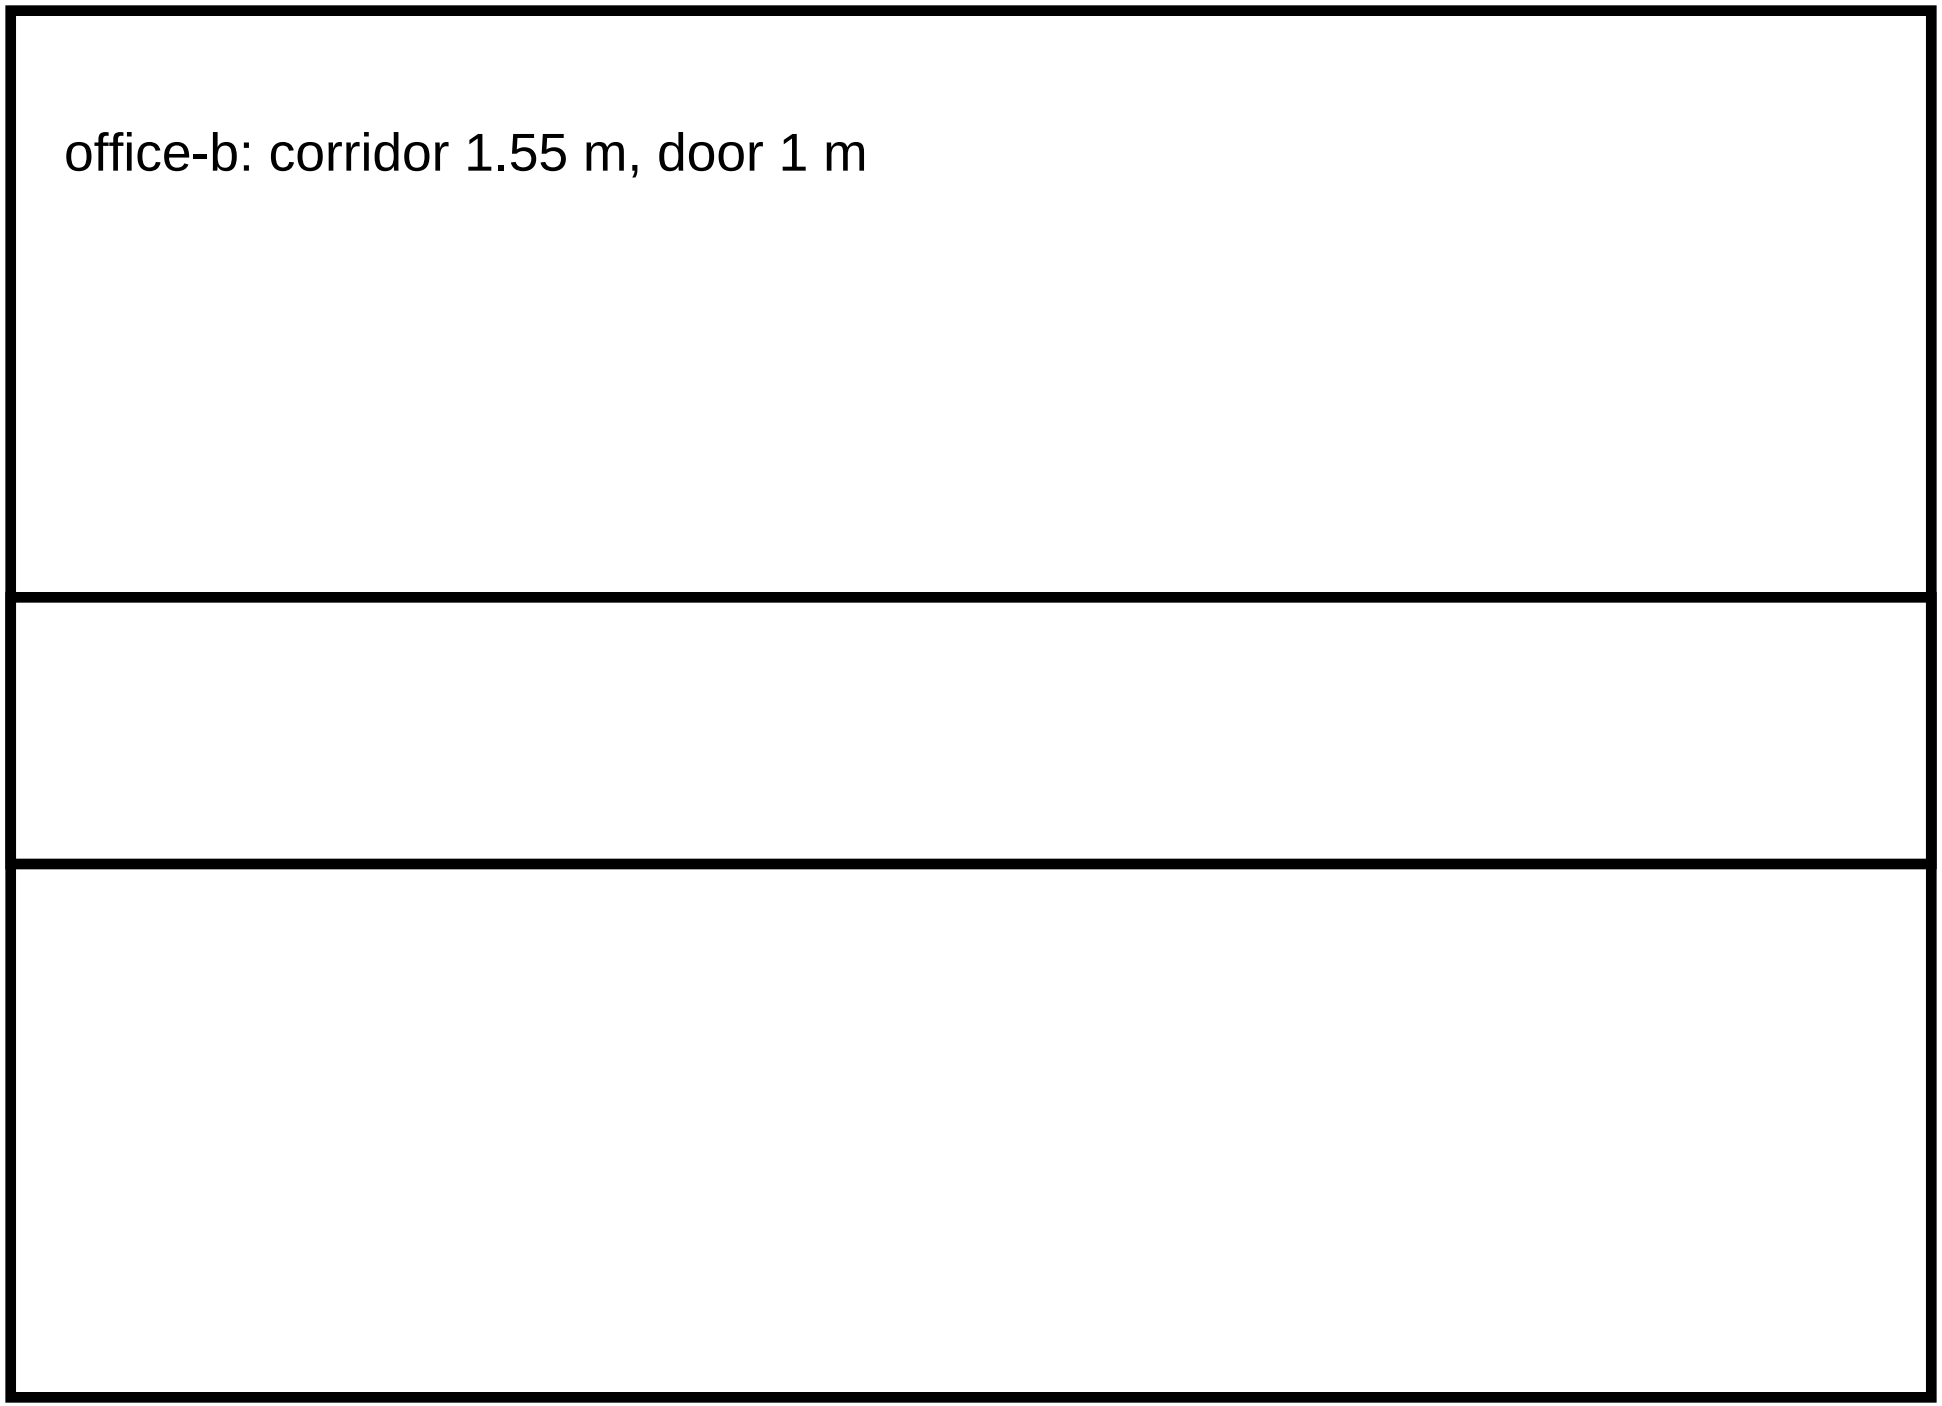
office-b: corridor 1.55 m, door 1 m